ТЕХНИЧЕСКИЙ ПЛАН
ЗДАНИЯ

(вид объекта недвижимости, в отношении которого подготовлен технический план, в родительном падеже)

Дата подготовки технического плана: 7 октября 2025 г.

(число, месяц, год)

Общие сведения о кадастровых работах

1. Технический план подготовлен в результате выполнения кадастровых работ в связи с:

изменением сведений о номере кадастрового квартала, количестве этажей, площади, материале стен, планировке и описании местоположения в пределах земельного участка здания с кадастровым номером 50:22:0000000:3900, по адресу: Московская область, р-н Люберецкий, р.п. Малаховка, ул. Маяковского, д. 18

ПУБЛИЧНАЯ ОБЕЗЛИЧЕННАЯ КОПИЯ

Персональные сведения заказчика и кадастрового инженера, контакты и реквизиты документа, удостоверяющего личность, удалены.

Чертежи, характеристики и экспликации сохранены. Порядок и число страниц соответствуют исходному файлу.

Эта копия не заменяет оригинал и не подтверждает регистрацию изменений в ЕГРН.

Исходные данные

Перечень документов, использованных при подготовке технического плана:

№ п/п	Реквизиты документа				
	Вид	Дата	Номер	Наименование	Иные сведения

1	2	3	4	5	6
3	Кадастровая выписка о здании, сооружении, объекте незавершѐнного строительства, выдан: Управление Федеральной службы государственной регистрации, кадастра и картографии по Московской области	23 июня 2025 г.	б/н	Выписка из ЕГРН об объекте недвижимости 50:22:0000000:3900	—
4	Кадастровая выписка о земельном участке, выдан: Филиал публично-правовой компании "Роскадастр" по Московской области	30 сентября 2025 г.	КУВИ-001/2025-183068433	Выписка из ЕГРН об объекте недвижимости 50:22:0030201:77	—
5	Материалы картографо-геодезического фонда, выдан: ФГБУ «Центр геодезии, картографии и ИПД»	2 июня 2022 г.	111/7071	Выписка о пунктах государственной геодезической сети	—
6	Договоры / соглашения	9 января 2023 г.	417БС2023	Договор об оказании услуг EFT-CORS	—

Сведения о пунктах геодезической сети и средствах измерений

1. Сведения о пунктах геодезической сети:

№ п/п	Вид геодезической сети	Название пункта геодезической сети и тип знака	Система координат пункта геодезической сети	Координаты пункта, м		Дата обследования 2 июня 2022 г.		
						Сведения о состоянии		
				X	Y	наружного знака пункта	центра пункта	марки центра пункта
1	2	3	4	5	6	7	8	9
1	геодезическая сеть специального назначения, сведения о наименовании (классе, разряде) геодезической сети отсутствуют. ГССН	Ногинск, Центр А	МСК-50	479 593,72	2 247 076,23	—	—	—

2. Сведения об использованных средствах измерений:

№ п/п	Наименование и обозначение типа средства измерений - прибора (инструмента, аппаратуры)	Заводской или серийный номер средства измерений	Реквизиты свидетельства о поверке прибора (инструмента, аппаратуры) (при наличии) и (или) срок действия поверки
1	2	3	4
1	Аппаратура геодезическая спутниковая EFT M2 GNSS	заводской номер PM11643695	Свидетельство о поверке №С-ГСХ/24-01-2025/404713960, выдано ООО "ЦИПСИ НАВГЕОТЕХ - ДИАГНОСТИКА" 24.01.2025 г., действительно до 23.01.2026 г.
2	Аппаратура геодезическая спутниковая EFT RS2	заводской номер RS20061	Свидетельство о поверке №С-ГСХ/28-03-2025/421393500, выдано ООО "ЦИПСИ НАВГЕОТЕХ - ДИАГНОСТИКА" 28.03.2025, действительно до 27.03.2026
3	Дальномер лазерный Leica DISTO X310	заводской номер 834626608	Свидетельство о поверке №С-ГСХ/30-04-2025/430336040, выдано ООО "ЦИПСИ НАВГЕОТЕХ - ДИАГНОСТИКА" 30.04.2025 г., действительно до 29.04.2026 г.

Описание местоположения объекта недвижимости

1. Описание местоположения здания, сооружения, объекта незавершенного строительства в границах земельного участка

1.1. Сведения о характерных точках контура объекта недвижимости

Система координат МСК-50 **Зона №** 2

Номер контура	Тип контура	Номера характерных точек контура	Метод определения координат	Координаты, м		R, м	Формулы, примененные для расчета средней квадратической погрешности определения координат характерных точек контура (Mt), м	Средняя квадратическая погреш-ность определения координат харак-терных точек контура (Mt), м	Глубина, высота расположения точки, м	
				X	Y				H1	H2
1	2	3	4	5	6	7	8	9	10	11
50:22:0000000:3900(1)										
50:22:0000000:3900(1)	подземный	1	Метод спутниковых геодезических измерений (определений)	458 167,65	2 221 280,85	—	Mt = √(m0^2 + m1^2) = √(0,04^2 + 0,09^2) = 0,10	0,10	—	—
		2		458 166,55	2 221 285,08	—			—	—
		3		458 167,53	2 221 285,34	—			—	—
		4		458 166,42	2 221 289,68	—			—	—
		5		458 165,41	2 221 289,42	—			—	—
		6		458 163,74	2 221 295,83	—			—	—
		7		458 150,91	2 221 292,67	—			—	—
		8		458 144,67	2 221 290,84	—			—	—
		9		458 114,08	2 221 282,92	—			—	—
		10		458 116,48	2 221 273,79	—			—	—
		11		458 115,31	2 221 273,48	—			—	—
		12		458 116,38	2 221 269,39	—			—	—
		13		458 117,55	2 221 269,70	—			—	—
		14		458 118,03	2 221 267,89	—			—	—
		15		458 161,06	2 221 279,22	—			—	—
		1		458 167,65	2 221 280,85	—			—	—
50:22:0000000:3900(2)										
50:22:0000000:3900(2)	наземный	16	Метод спутниковых геодезических измерений (определений)	458 167,79	2 221 280,32	—	Mt = √(m0^2 + m1^2) = √(0,04^2 + 0,09^2) = 0,10	0,10	—	—
		2		458 166,55	2 221 285,08	—			—	—
		17		458 167,26	2 221 285,27	—			—	—
		18		458 167,36	2 221 284,90	—			—	—
		19		458 167,63	2 221 284,97	—			—	—
		4		458 166,42	2 221 289,68	—			—	—
		5		458 165,41	2 221 289,42	—			—	—
		20		458 163,61	2 221 296,34	—			—	—
		21		458 163,22	2 221 296,24	—			—	—
		22		458 163,35	2 221 295,74	—			—	—
		23		458 157,34	2 221 294,26	—			—	—
		24		458 157,28	2 221 294,51	—			—	—
		25		458 157,01	2 221 294,44	—			—	—
		26		458 157,07	2 221 294,19	—			—	—
		7		458 150,91	2 221 292,67	—			—	—
		27		458 150,85	2 221 292,93	—			—	—
		28		458 150,78	2 221 292,91	—			—	—
		29		458 150,39	2 221 294,12	—			—	—
		30		458 148,49	2 221 294,75	—			—	—
		31		458 145,68	2 221 293,93	—			—	—
		32		458 144,36	2 221 292,31	—			—	—
		33		458 144,62	2 221 291,08	—			—	—
		34		458 139,02	2 221 289,60	—			—	—
		35		458 138,75	2 221 289,53	—			—	—
		36		458 138,81	2 221 289,29	—			—	—
		37		458 132,71	2 221 287,72	—			—	—
		38		458 132,64	2 221 287,97	—			—	—
		39		458 132,39	2 221 287,90	—			—	—

1	2	3	4	5	6	7	8	9	10	11
50:22:0000000:3900(2)	наземный	40	Метод спутниковых геодезических измерений (определений)	458 132,46	2 221 287,64	—	Mt = √(m0^2 + m1^2) = √(0,04^2 + 0,09^2) = 0,10	0,10	—	—
		41		458 126,76	2 221 286,19	—			—	—
		42		458 126,69	2 221 286,46	—			—	—
		43		458 126,42	2 221 286,39	—			—	—
		44		458 126,49	2 221 286,12	—			—	—
		45		458 120,64	2 221 284,68	—			—	—
		46		458 120,57	2 221 284,96	—			—	—
		47		458 120,30	2 221 284,88	—			—	—
		48		458 120,37	2 221 284,61	—			—	—
		49		458 114,39	2 221 283,00	—			—	—
		50		458 114,26	2 221 283,52	—			—	—
		51		458 113,94	2 221 283,44	—			—	—
		10		458 116,48	2 221 273,79	—			—	—
		11		458 115,31	2 221 273,48	—			—	—
		52		458 116,55	2 221 268,74	—			—	—
		53		458 116,82	2 221 268,80	—			—	—
		54		458 116,64	2 221 269,46	—			—	—
		13		458 117,55	2 221 269,70	—			—	—
		55		458 118,17	2 221 267,36	—			—	—
		56		458 118,45	2 221 267,43	—			—	—
		57		458 118,31	2 221 267,96	—			—	—
		58		458 124,31	2 221 269,55	—			—	—
		59		458 124,38	2 221 269,28	—			—	—
		60		458 124,65	2 221 269,34	—			—	—
		61		458 124,58	2 221 269,62	—			—	—
		62		458 130,42	2 221 271,15	—			—	—
		63		458 130,48	2 221 270,88	—			—	—
		64		458 130,76	2 221 270,95	—			—	—
		65		458 130,69	2 221 271,22	—			—	—
		66		458 136,46	2 221 272,74	—			—	—
		67		458 136,53	2 221 272,47	—			—	—
		68		458 136,80	2 221 272,54	—			—	—
		69		458 136,73	2 221 272,81	—			—	—
		70		458 142,53	2 221 274,34	—			—	—
		71		458 142,60	2 221 274,07	—			—	—
		72		458 142,87	2 221 274,14	—			—	—
		73		458 142,80	2 221 274,41	—			—	—
		74		458 148,67	2 221 275,96	—			—	—
		75		458 148,74	2 221 275,69	—			—	—
		76		458 149,01	2 221 275,76	—			—	—
		77		458 148,94	2 221 276,03	—			—	—
		78		458 154,59	2 221 277,52	—			—	—
		79		458 154,66	2 221 277,24	—			—	—
		80		458 154,93	2 221 277,32	—			—	—
		81		458 154,86	2 221 277,59	—			—	—
		82		458 160,79	2 221 279,15	—			—	—
		83		458 160,86	2 221 278,88	—			—	—
		84		458 161,13	2 221 278,95	—			—	—
		15		458 161,06	2 221 279,22	—			—	—
		85		458 167,10	2 221 280,72	—			—	—
		86		458 167,29	2 221 280,20	—			—	—
		16		458 167,79	2 221 280,32	—			—	—
50:22:0000000:3900(3)										
50:22:0000000:3900(3)	надземный	16	Метод спутниковых геодезических измерений (определений)	458 167,79	2 221 280,32	—	Mt = √(m0^2 + m1^2) = √(0,04^2 + 0,09^2) = 0,10	0,10	—	—
		20		458 163,61	2 221 296,34	—			—	—
		21		458 163,22	2 221 296,24	—			—	—
		22		458 163,35	2 221 295,74	—			—	—
		23		458 157,34	2 221 294,26	—			—	—
		24		458 157,28	2 221 294,51	—			—	—

1	2	3	4	5	6	7	8	9	10	11
50:22:0000000:3900(3)	надземный	25	Метод спутниковых геодезических измерений (определений)	458 157,01	2 221 294,44	—	Mt = √(m0^2 + m1^2) = √(0,04^2 + 0,09^2) = 0,10	0,10	—	—
		26		458 157,07	2 221 294,19	—			—	—
		7		458 150,91	2 221 292,67	—			—	—
		27		458 150,85	2 221 292,93	—			—	—
		28		458 150,78	2 221 292,91	—			—	—
		29		458 150,39	2 221 294,12	—			—	—
		30		458 148,49	2 221 294,75	—			—	—
		31		458 145,68	2 221 293,93	—			—	—
		32		458 144,36	2 221 292,31	—			—	—
		8		458 144,67	2 221 290,84	—			—	—
		87		458 139,08	2 221 289,36	—			—	—
		34		458 139,02	2 221 289,60	—			—	—
		35		458 138,75	2 221 289,53	—			—	—
		36		458 138,81	2 221 289,29	—			—	—
		37		458 132,71	2 221 287,72	—			—	—
		38		458 132,64	2 221 287,97	—			—	—
		39		458 132,39	2 221 287,90	—			—	—
		40		458 132,46	2 221 287,64	—			—	—
		41		458 126,76	2 221 286,19	—			—	—
		42		458 126,69	2 221 286,46	—			—	—
		43		458 126,42	2 221 286,39	—			—	—
		44		458 126,49	2 221 286,12	—			—	—
		45		458 120,64	2 221 284,68	—			—	—
		46		458 120,57	2 221 284,96	—			—	—
		47		458 120,30	2 221 284,88	—			—	—
		48		458 120,37	2 221 284,61	—			—	—
		49		458 114,39	2 221 283,00	—			—	—
		50		458 114,26	2 221 283,52	—			—	—
		51		458 113,94	2 221 283,44	—			—	—
		55		458 118,17	2 221 267,36	—			—	—
		56		458 118,45	2 221 267,43	—			—	—
		57		458 118,31	2 221 267,96	—			—	—
		58		458 124,31	2 221 269,55	—			—	—
		59		458 124,38	2 221 269,28	—			—	—
		60		458 124,65	2 221 269,34	—			—	—
		61		458 124,58	2 221 269,62	—			—	—
		62		458 130,42	2 221 271,15	—			—	—
		63		458 130,48	2 221 270,88	—			—	—
		64		458 130,76	2 221 270,95	—			—	—
		65		458 130,69	2 221 271,22	—			—	—
		66		458 136,46	2 221 272,74	—			—	—
		67		458 136,53	2 221 272,47	—			—	—
		68		458 136,80	2 221 272,54	—			—	—
		69		458 136,73	2 221 272,81	—			—	—
		70		458 142,53	2 221 274,34	—			—	—
		71		458 142,60	2 221 274,07	—			—	—
		72		458 142,87	2 221 274,14	—			—	—
		73		458 142,80	2 221 274,41	—			—	—
		74		458 148,67	2 221 275,96	—			—	—
		75		458 148,74	2 221 275,69	—			—	—
		76		458 149,01	2 221 275,76	—			—	—
		77		458 148,94	2 221 276,03	—			—	—
		78		458 154,59	2 221 277,52	—			—	—
		79		458 154,66	2 221 277,24	—			—	—
		80		458 154,93	2 221 277,32	—			—	—
		81		458 154,86	2 221 277,59	—			—	—
		82		458 160,79	2 221 279,15	—			—	—
		83		458 160,86	2 221 278,88	—			—	—
		84		458 161,13	2 221 278,95	—			—	—

1	2	3	4	5	6	7	8	9	10	11
		15		458 161,06	2 221 279,22	—			—	—
		85		458 167,10	2 221 280,72	—			—	—
		86		458 167,29	2 221 280,20	—			—	—
		16		458 167,79	2 221 280,32	—			—	—
50:22:0000000:3900(4)										
50:22:0000000:3900(4)	надземный	88	Метод спутниковых геодезических измерений (определений)	458 118,22	2 221 267,16	—	Mt = √(m0^2 + m1^2) = √(0,04^2 + 0,09^2) = 0,10	0,10	—	—
		93		458 167,84	2 221 280,12	—			—	—
		92		458 163,56	2 221 296,55	—			—	—
		91		458 150,69	2 221 293,20	—			—	—
		29		458 150,39	2 221 294,12	—			—	—
		30		458 148,49	2 221 294,75	—			—	—
		31		458 145,68	2 221 293,93	—			—	—
		32		458 144,36	2 221 292,31	—			—	—
		90		458 144,51	2 221 291,60	—			—	—
		89		458 113,89	2 221 283,64	—			—	—
		88		458 118,22	2 221 267,16	—			—	—

1.2. Сведения о предельных глубине и высоте строительных конструкций объекта недвижимости

Предельная глубина строительных конструкций объекта недвижимости, м	—
Предельная высота строительных конструкций объекта недвижимости, м	—

1.3. Сведения о характерных точках пересечения контура объекта недвижимости с контуром (контурами) иных зданий, сооружений, объектов незавершенного строительства

Система координат — **Зона №** —

Номер контура	Тип контура	Номера характерных точек контура	Метод определения координат	Координаты, м		Формулы, примененные для расчета средней квадратической погрешности определения координат характерных точек контура (Mt), м	Средняя квадратическая погрешность определения координат характерных точек контура (Mt), м	Глубина, высота, м		Кадастровый номер
				X	Y			H_1	H_2	
1	2	3	4	5	6	7	8	9	10	11
—	—	—	—	—	—	—	—	—	—	—

2. Описание местоположения машино-места

Обозначение машино-места (номер) —

2.1. Сведения о расстояниях

2.1.1. Сведения о расстояниях от специальных меток до характерных точек границ машино-места

№ п/п специальной метки	№ п/п характерной точки границы машино-места	Расстояние, м
1	2	3
—	—	—

2.1.2. Сведения о расстояниях между характерными точками границ машино-места

№ п/п характерной точки границы машино-места	№ п/п характерной точки границы машино-места	Расстояние, м
1	2	3
—	—	—

2.2. Сведения о координатах специальных меток (при наличии)

№ п/п специальной метки	Координаты, м		Формулы, примененные для расчета средней квадратической погрешности определения координат специальных меток (Mt), м	Средняя квадратическая погрешность определения координат (Mt), м
	X	Y		
1	2	3	4	5
—	—	—	—	—

2.3. Сведения о характерных точках границ помещения, в котором расположено машино-место

Номера характерных точек границ помещения	Координаты, м		Формулы, примененные для расчета средней квадратической погрешности определения координат характерных точек контура (Mt), м	Средняя квадратическая погрешность определения координат характерных точек контура (Mt), м
	X	Y		

1	2	3	4	5
—	—	—	—	—

Характеристики объекта недвижимости

№ п/п	Наименование характеристики	Значение характеристики
1	2	3
1	**Вид объекта недвижимости**	**Здание**
2	**Кадастровый номер объекта недвижимости**	**50:22:0000000:3900**
3	**Ранее присвоенный государственный учетный номер объекта недвижимости (кадастровый, инвентарный или условный номер)**	**инвентарный номер 125:039-9327; условный номер 50-50-22/005/2012-278**
4	**Кадастровые номера исходного(ых) объекта(ов) недвижимости (из которого (которых) образован объект недвижимости)**	**—**
5	**Номер кадастрового квартала (кадастровых кварталов), в котором (которых) находится объект недвижимости**	**50:22:0030201**
5.1	**Номера кадастровых округов**	**—**
6	**Кадастровые номера иных объектов недвижимости, в границах которых или в которых расположен объект недвижимости**	**—**
6.1	Кадастровый номер земельного участка (земельных участков), в границах которого (которых) расположены здание, сооружение или объект незавершенного строительства	**50:22:0030201:77**
6.2	Кадастровый номер здания или сооружения, в котором расположено помещение или машино-место	**—**
6.3	Кадастровый номер квартиры, в которой расположена комната	**—**
6.4	Кадастровые номера помещений, машино-мест, расположенных в здании, сооружении	**—**
7	**Кадастровый номер единого недвижимого комплекса или предприятия как имущественного комплекса, если объект недвижимости входит в состав таких объектов и (или) право на него (в том числе право аренды) входит в состав предприятия как имущественного комплекса**	**—**
8	**Адрес объекта недвижимости**	**—**
	Местоположение объекта недвижимости	**Московская область, р-н Люберецкий, р.п. Малаховка, ул. Маяковского, д. 18**
	Дополнение местоположения объекта недвижимости	**—**
9	**Наименование водного объекта, на котором (в акватории или части акватории которого) расположено гидротехническое сооружение**	**—**
10	**Назначение здания, сооружения, помещения, единого недвижимого комплекса**	**Жилое**
	Проектируемое назначение объекта незавершенного строительства	**—**
11	**Вид (виды) разрешенного использования здания, сооружения, помещения**	**—**
12	**Наименование здания, сооружения, помещения, единого недвижимого комплекса**	**Здание жилого назначения (общежитие)**
13	**Количество этажей объекта недвижимости**	**4**
	в том числе подземных	**1**
14	**Материал наружных стен здания**	**Кирпичные**
15	**Год ввода объекта недвижимости в эксплуатацию по завершении его строительства**	**—**
16	**Год завершения строительства объекта недвижимости**	**1975**
17	**Век (период) постройки объекта недвижимости**	**—**
18	**Площадь объекта недвижимости (Р), м², и средняя квадратическая погрешность ее определения, м²**	**2967,4 ± 0,92**

<table>
<tr><td rowspan="2">19</td><td rowspan="2">Основная(ые) характеристика(и) сооружения и ее (их) значение(я)</td><td>Тип</td><td>Значение</td><td>Единицы измерения</td></tr>
<tr><td>—</td><td>—</td><td>—</td></tr>
<tr><td>20</td><td>Степень готовности объекта незавершенного строительства, %</td><td colspan="3">—</td></tr>
<tr><td>21</td><td>Основная характеристика объекта незавершенного строительства и ее проектируемое значение</td><td colspan="3">—</td></tr>
<tr><td>22</td><td>Номер, тип этажа, на котором (которых) расположено помещение</td><td colspan="3">—</td></tr>
<tr><td>23</td><td>Номер, тип этажа, на котором расположено машино-место</td><td colspan="3">—</td></tr>
<tr><td>24</td><td>Обозначение (номер) помещения, машино-места на поэтажном плане</td><td colspan="3">—</td></tr>
<tr><td>25</td><td>Вид жилого помещения (квартира, комната (в квартире), если жилое помещение расположено в многоквартирном доме</td><td colspan="3">—</td></tr>
<tr><td>26</td><td>Сведения о том, что помещение предназначено для обслуживания всех остальных помещений и (или) машино-мест в здании, сооружении или помещение относится к общему имуществу в многоквартирном доме</td><td colspan="3">—</td></tr>
<tr><td>27</td><td>Сведения об отнесении помещения к специализированному жилищному фонду или к жилым помещениям наемного дома социального использования или наемного дома коммерческого использования</td><td colspan="3">—</td></tr>
<tr><td rowspan="2">28</td><td rowspan="2">Сведения об объектах недвижимости, входящих в состав единого недвижимого комплекса (включаемых и (или) исключаемых из его состава)</td><td>№ п/п</td><td>Вид объекта недвижимости</td><td>Кадастровый номер</td></tr>
<tr><td>—</td><td>—</td><td>—</td></tr>
<tr><td rowspan="2">29</td><td rowspan="2">Сведения об объектах недвижимости, входящих в состав сооружения, представляющего собой сложную вещь</td><td>№ п/п</td><td>Вид объекта недвижимости</td><td>Тип и значение основной характеристики</td></tr>
<tr><td>—</td><td>—</td><td>—</td></tr>
<tr><td>30</td><td>Сведения о включении объекта недвижимости в единый государственный реестр объектов культурного наследия (памятников истории и культуры) народов Российской Федерации</td><td colspan="3"></td></tr>
<tr><td>30.1</td><td>Регистрационный номер, вид и наименование объекта недвижимости в едином государственном реестре объектов культурного наследия (памятников истории и культуры) народов Российской Федерации либо регистрационный номер учетной карты объекта, представляющего собой историко-культурную ценность, вид и наименование выявленного объекта культурного наследия</td><td colspan="3">—</td></tr>
<tr><td>30.2</td><td>Реквизиты решений Правительства Российской Федерации, органов охраны объектов культурного наследия о включении объекта недвижимости в единый государственный реестр объектов культурного наследия (памятников истории и культуры) народов Российской Федерации либо об отнесении объекта недвижимости к выявленным объектам культурного наследия, подлежащим государственной охране</td><td colspan="3">—</td></tr>
<tr><td>30.3</td><td>Реквизиты документа, на основании которого установлены требования к сохранению, содержанию и использованию объектов культурного наследия (памятников истории и культуры) народов Российской Федерации, требования к обеспечению доступа к таким объектам либо выявленному объекту культурного наследия</td><td colspan="3">—</td></tr>
</table>

Заключение кадастрового инженера

Технический план здания подготовлен по результатам натурного обследования в целях предоставления в судебные органы достоверного и подробного описания здания в связи с изменением сведений о номере кадастрового квартала, количестве этажей, площади, материале стен, планировке и описании местоположения в пределах земельного участка здания с кадастровым номером 50:22:0000000:3900, по адресу: Московская область, р-н Люберецкий, р.п. Малаховка, ул. Маяковского, д. 18.

Технический план подготовлен в соответствии с Требованиями к подготовке технического плана, утверждѐнных Приказом Росреестра от 15.03.2022 г. № П/0082 (далее – Требования).

В соответствии с п. 35 Требований контура здания проведены по внешним границам строительных конструкций здания. Здание описано четырьмя контурами: подземным контуром 1 описан Цокольный этаж здания, наземным контуром 2 описан Первый этаж здания, надземными контурами 3 и 4 описаны соответственно Второй и Мансардный этажи здания.

Площадь объекта недвижимости в данном техническом плане установлена согласно Требованиям к определению площади здания, сооружения и помещения, машино-места, утверждѐнным Приказом Росреестра от 23.10.2020 № П/0393, составляет 2967.4 кв.м.

Согласно п.5 Требований, площадь нежилого или жилого здания, сооружения определяется как сумма площадей всех надземных и подземных этажей (включая технический, мансардный, цокольный и иные), а также эксплуатируемой кровли.

Согласно п.10.2. Требований к определению площади здания, сооружения и помещения, машино-места утверждѐнных Приказом Росреестра от 23.10.2020 № П/0393, площадь этажа нежилого здания определяется в пределах внутренних поверхностей наружных стен.

В Экспликации, содержащейся в данном техническом плане, указаны как площади комнат, расположенных в здании, так и общая площадь здания, установленная в соответствии с Требованиями по внутренней поверхности наружных стен.

Разница между общей площадью здания и суммой площадей всех комнат, расположенных в здании, является площадью, занятой внутренними стенами и перегородками. При этом площадь, занятая внутренними стенами и перегородками, входит в общую площадь здания, которая подлежит внесению в ЕГРН.

Разница между содержащимся в ЕГРН значением общей площади здания отражает не только наличие Мансардного этажа, но также иной принцип подсчѐта общей площади, включающий в общую площадь внутренние стены и перегородки, а не только сумму площадей помещений.

В соответствии с Приказом Росреестра от 23.10.2020 № П/0393 средняя квадратическая погрешность определения площади здания определялась по формуле, описанной в п. 4 раздела "Рекомендуемые формулы расчета погрешности определения (вычисления) площади здания, сооружения помещения, машино-места".

Средняя квадратическая погрешность определения площади здания составляет:

Цокольный этаж:

mp_Цэт=SQR(SUM(mf^2))=SQR(SUM((0,01/2SQR(0,16^2+1,78^2))^2+(0,01/2SQR(47,43^2+0,16^2))^2+(0,01/2SQR(14,29^2+47,43^2))^2+(0,01/2SQR(10,34^2+0,08^2))^2+(0,01/2SQR(11,7^2+0,13^2))^2+(0,01/2SQR(0,54^2+3,76^2))^2+(0,01/2SQR(14,4^2+24,79^2))^2+(0,01/2SQR =

0,488;

1 этаж:

mp_1эт=SQR(SUM(mf^2))=SQR(SUM((0,01/2SQR(0,17^2+1,78^2))^2+(0,01/2SQR(47,85^2+0,27^2))^2+(0,01/2SQR(9,26^2+47,84^2))^2+(0,01/2SQR(12,38^2+5,31^2))^2+(0,01/2SQR(0,58^2+5,2^2))^2+(0,01/2SQR(0,98^2+0,11^2))^2+(0,01/2SQR(0,18^2+0,71^2))^2+(0,01/2SQR(0,19^2+0,84^2))^2+(0,01/2SQR(2,74^2+0,08^2))^2+(0,01/2SQR(1,74^2+0,03^2))^2+(0,01/2SQR(1,72^2+0,08^2))^2+(0,01/2SQR(1,8^2+0,04^2))^2+(0,01/2SQR(0,4^2+1,73^2))^2+(0,01/2SQR(0,08^2+3,8^2))^2+(0,01/2SQR(14,35^2+9,27^2))^2+(0,01/2SQR(1,86^2+13,48^2))^2+(0,01/2SQR(48,68^2+0,12^2))^2+(0,01/2SQR(1,11^2+0,08^2))^2+(0,01/2SQR(1,71^2+1,76^2))^2+(0,01/2SQR(2,74^2+2,88^2))^2+(0,01/2SQR(0,08^2+1,33^2))^2+(0,01/2SQR(1,81^2+1,48^2))^2+(0,01/2SQR(16^2+13,94^2))^2+(0,01/2SQR(0,05^2+9,01^2))^2+(0,01/2SQR(14,01^2+26,71^2))^2+(0,01/2SQR(0,08^2+4,31^2))^2+(0,01/2SQR(27,17^2+3,18^2))^2+(0,01/2SQR(38,25^2+2,27^2))^2+(0,01/2SQR(3,35^2+5,16^2))^2)) = 0,536;

2 этаж:

mp_2эт=SQR(SUM(mf^2))=SQR(SUM((0,01/2SQR(25,03^2+0,06^2))^2+(0,01/2SQR(8,02^2+25,36^2))^2+(0,01/2SQR(6,35^2+0,03^2))^2+(0,01/2SQR(2,94^2+0,23^2))^2+(0,01/2SQR(0,23^2+2,94^2))^2+(0,01/2SQR(1,72^2+1,84^2))^2+(0,01/2SQR(0,16^2+2,34^2))^2+(0,01/2SQR(1,78^2+1,49^2))^2+(0,01/2SQR(0,36^2+5,97^2))^2+(0,01/2SQR(14,43^2+25,39^2))^2+(0,01/2SQR(24,9^2+14,43^2))^2+(0,01/2SQR(6,55^2+25,34^2))^2+(0,01/2SQR(7,1^2+0^2))^2+(0,01/2SQR(4,28^2+3,31^2))^2+(0,01/2SQR(1,74^2+5,85^2))^2+(0,01/2SQR(14,44^2+5,95^2))^2+(0,01/2SQR(3,05^2+14,51^2))^2+(0,01/2SQR(16,14^2+5,47^2))^2+(0,01/2SQR(26,65^2+5,47^2))^2))= 0,368;

Мансардный этаж:

mp_Мэт=SQR(SUM(mf^2))=SQR(SUM((0,01/2SQR(14,74^2+50,03^2))^2+(0,01/2SQR(1,72^2+1,8^2))^2+(0,01/2SQR(0,15^2+2,3^2))^2+(0,01/2SQR(1,78^2+1,49^2))^2+(0,01/2SQR(0,28^2+0,97^2))^2+(0,01/2SQR(3,04^2+0,08^2))^2+(0,01/2SQR(14,73^2+2,94^2))^2+(0,01/2SQR(52,16^2+13,3^2))^2+(0,01/2SQR(4,28^2+3,26^2))^2+(0,01/2SQR(1,01^2+5,02^2))^2+(0,01/2SQR(12,88^2+0,01^2))^2+(0,01/2SQR(34,21^2+0^2))^2+(0,01/2SQR(1^2+5,52^2))^2))=0,427.

Таким образом, средняя квадратическая погрешность определения площади здания составляет:

mp=msSQR (mp_Цэт^2 + mp_1эт ^2 + mp_2эт ^2 + mp_Мэт ^2) = 0,01SQR (0,488^2+0,536^2+0,368^2+0,427^2) = 0,92 кв.м.

На планах этажей здание сориентировано фасадом параллельно нижнему краю листа.

В соответствии с п. 50 Требований, в техническом плане должны быть заполнены только изменяемые характеристики здания, подлежащие внесению в ЕГРН. Но так как Технический план подготовлен для направления в судебные органы, для наиболее полного описания объекта недвижимости в нѐм заполнены все характеристики.

Для определения планового местоположения характерных точек объекта кадастровых работ использовалась постоянно действующая базовая станция «Ногинск» - пункт государственной геодезической сети специального назначения.


Пункт «Ногинск» является пунктом государственной геодезической сети, что подтверждается выпиской ФГБУ «Центр геодезии, картографии и ИПД» от 02.06.2022 №111/7071, входит в состав федеральной спутниковой дифференциальной сети базовых станций EFT-CORS, оператором которой является ИП Дронов А.В. (ИНН 507404132344), с

Заключение кадастрового инженера

которым у кадастрового инженера заключѐн договор на использование измерительной и корректирующей информации от 09.01.2023 № 417БС2023.

В связи с использованием пункта сети дифференциальных геодезических станций в техническом плане строка, предусмотренная для отражения сведений "о дате обследования", не заполнена.

Схема геодезических построений

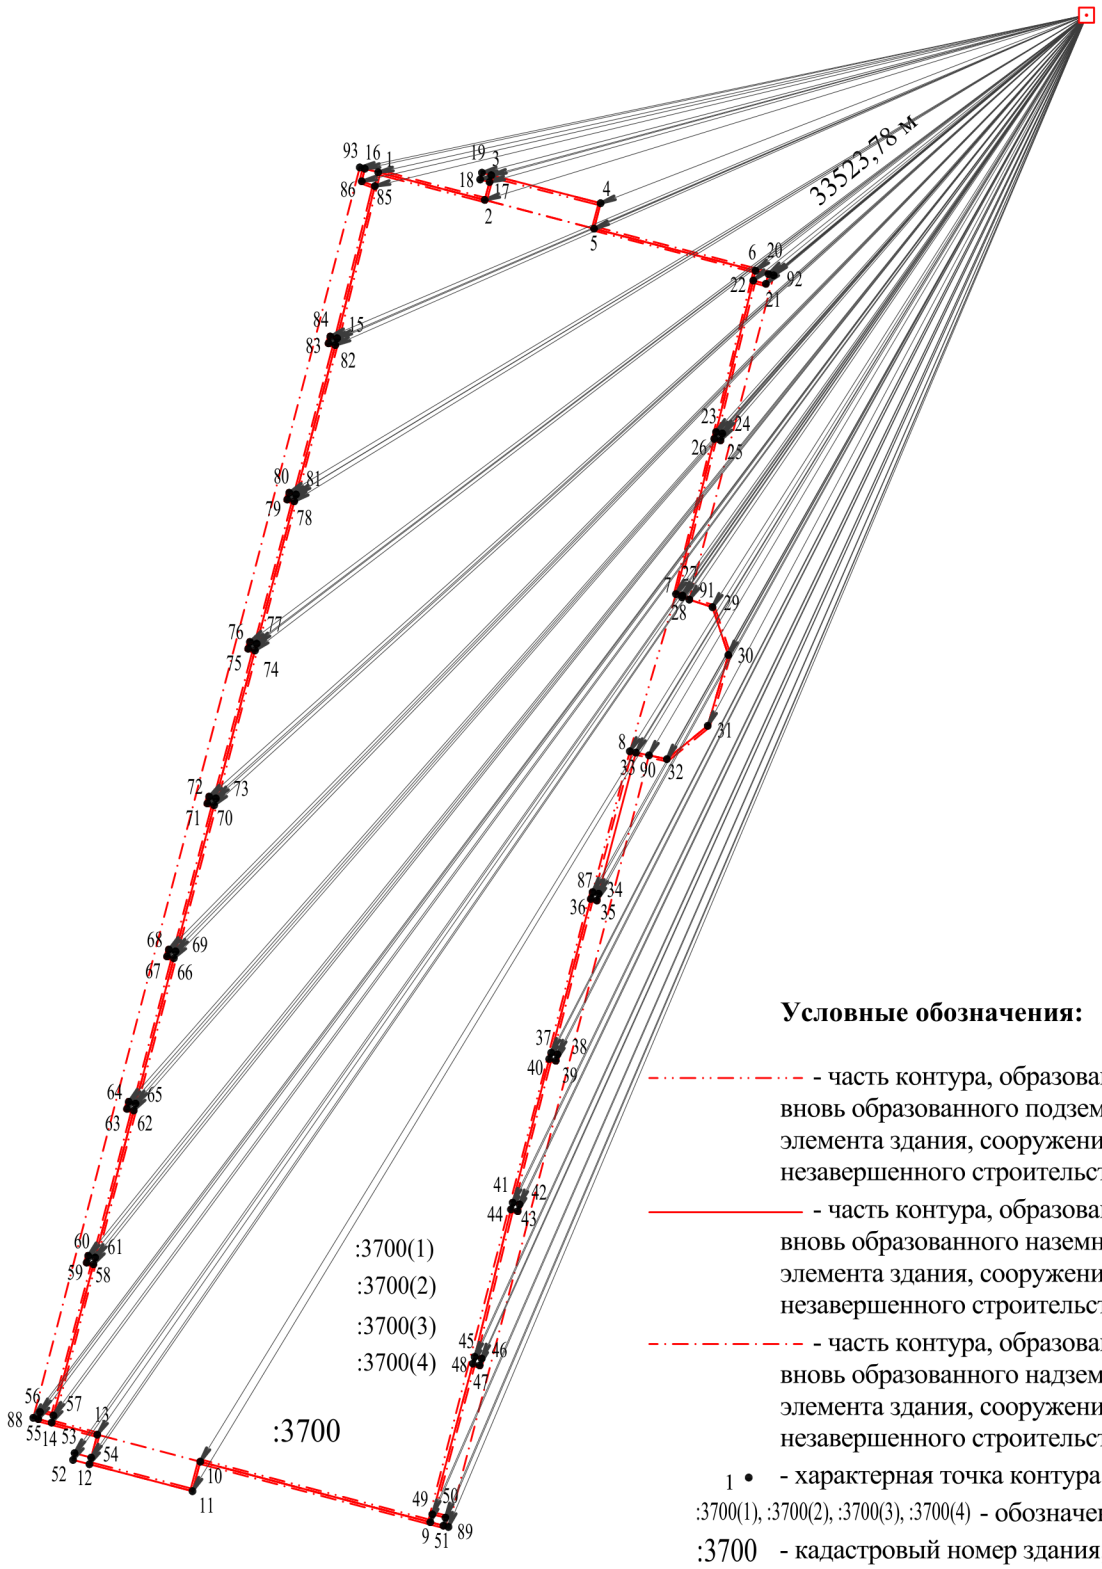

Условные обозначения:

- часть контура, образованного проекцией вновь образованного подземного конструктивного элемента здания, сооружения, объекта незавершенного строительства;

- часть контура, образованного проекцией вновь образованного наземного конструктивного элемента здания, сооружения, объекта незавершенного строительства;

- часть контура, образованного проекцией вновь образованного надземного конструктивного элемента здания, сооружения, объекта незавершенного строительства;

1 • - характерная точка контура здания;

:3700(1), :3700(2), :3700(3), :3700(4) - обозначение контура здания;


:3700 - кадастровый номер здания;

Ногинск ⊡ - пункт ГССН (сети дифференциальных геодезических станций);

- направления полярных измерений положения поворотных точек границы земельных участков;

33523,78 м - расстояние от пункта ГССН, на котором расположена базовая станция, до ближайшей характерной точки контура объекта кадастровых работ.

Схема расположения здания (части здания) на земельном участке

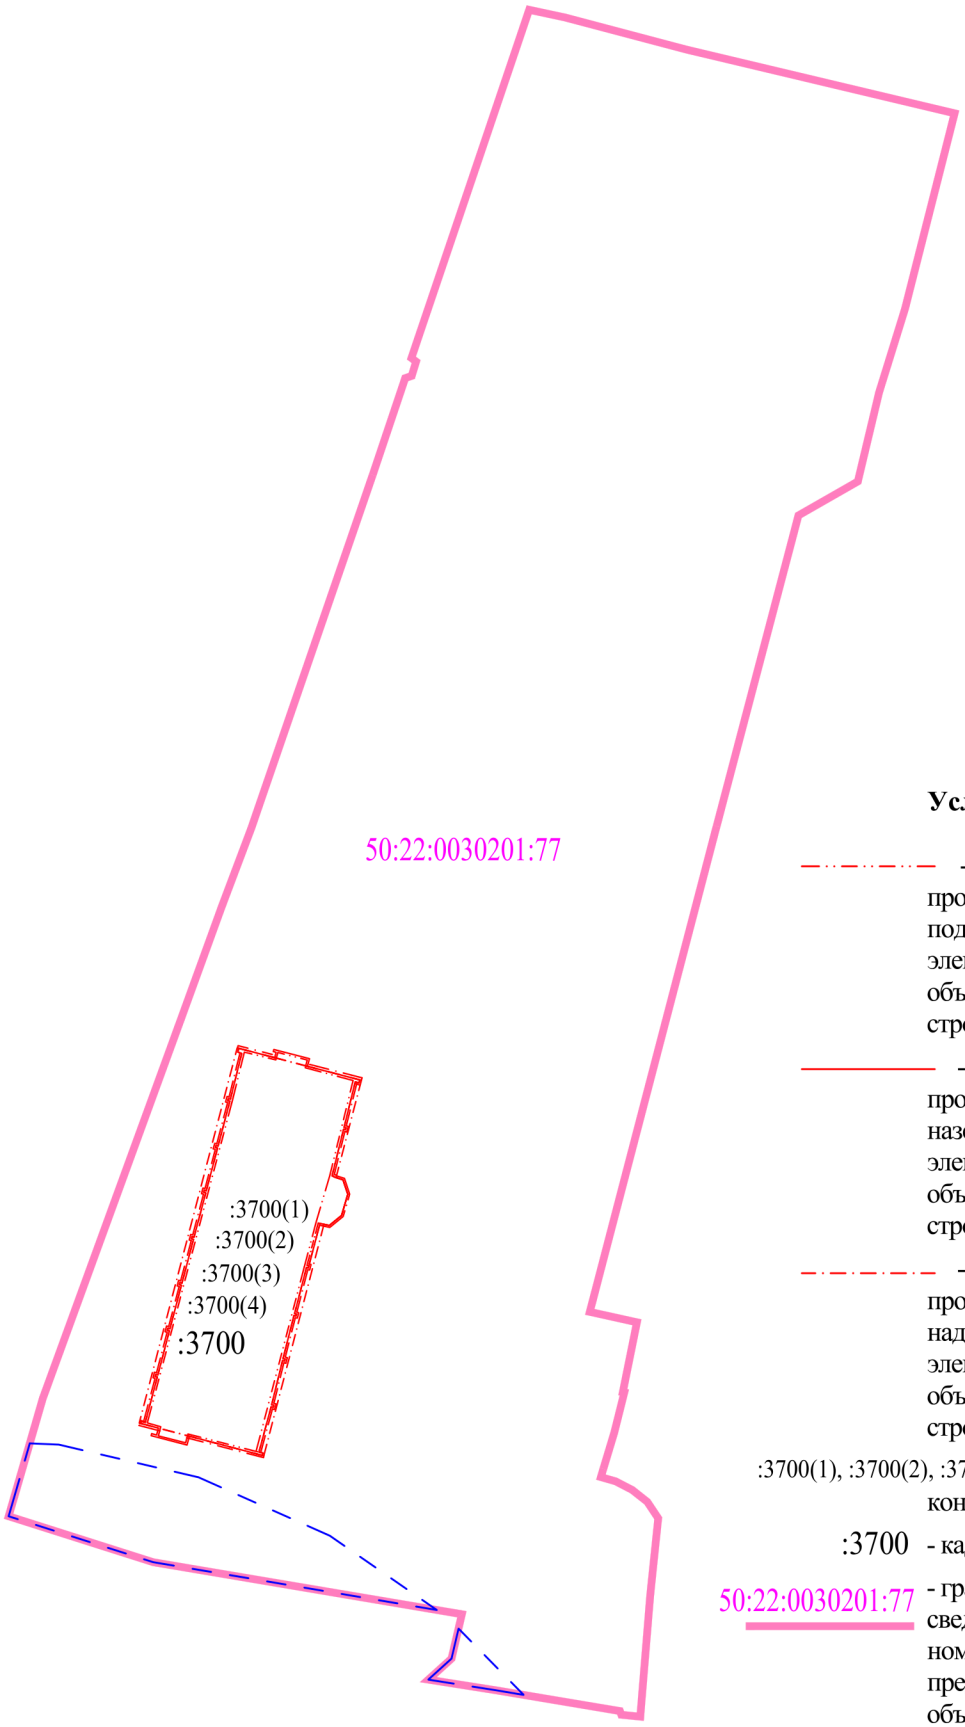

Условные обозначения:

- часть контура, образованного проекцией вновь образованного подземного конструктивного элемента здания, сооружения, объекта незавершенного строительства;

- часть контура, образованного проекцией вновь образованного наземного конструктивного элемента здания, сооружения, объекта незавершенного строительства;

- часть контура, образованного проекцией вновь образованного надземного конструктивного элемента здания, сооружения, объекта незавершенного строительства;

:3700(1), :3700(2), :3700(3), :3700(4) - обозначение контура здания;


:3700 - кадастровый номер здания;

50:22:0030201:77 - граница земельного участка по сведениям ЕГРН и кадастровый номер земельного участка, в пределах которого расположен объект недвижимости;

- части земельного участка, в пределах которого расположен объект недвижимости, по сведениям ЕГРН.

Масштаб 1:1000

Чертеж контура здания, сооружения (части объекта недвижимости), объекта незавершенного строительства

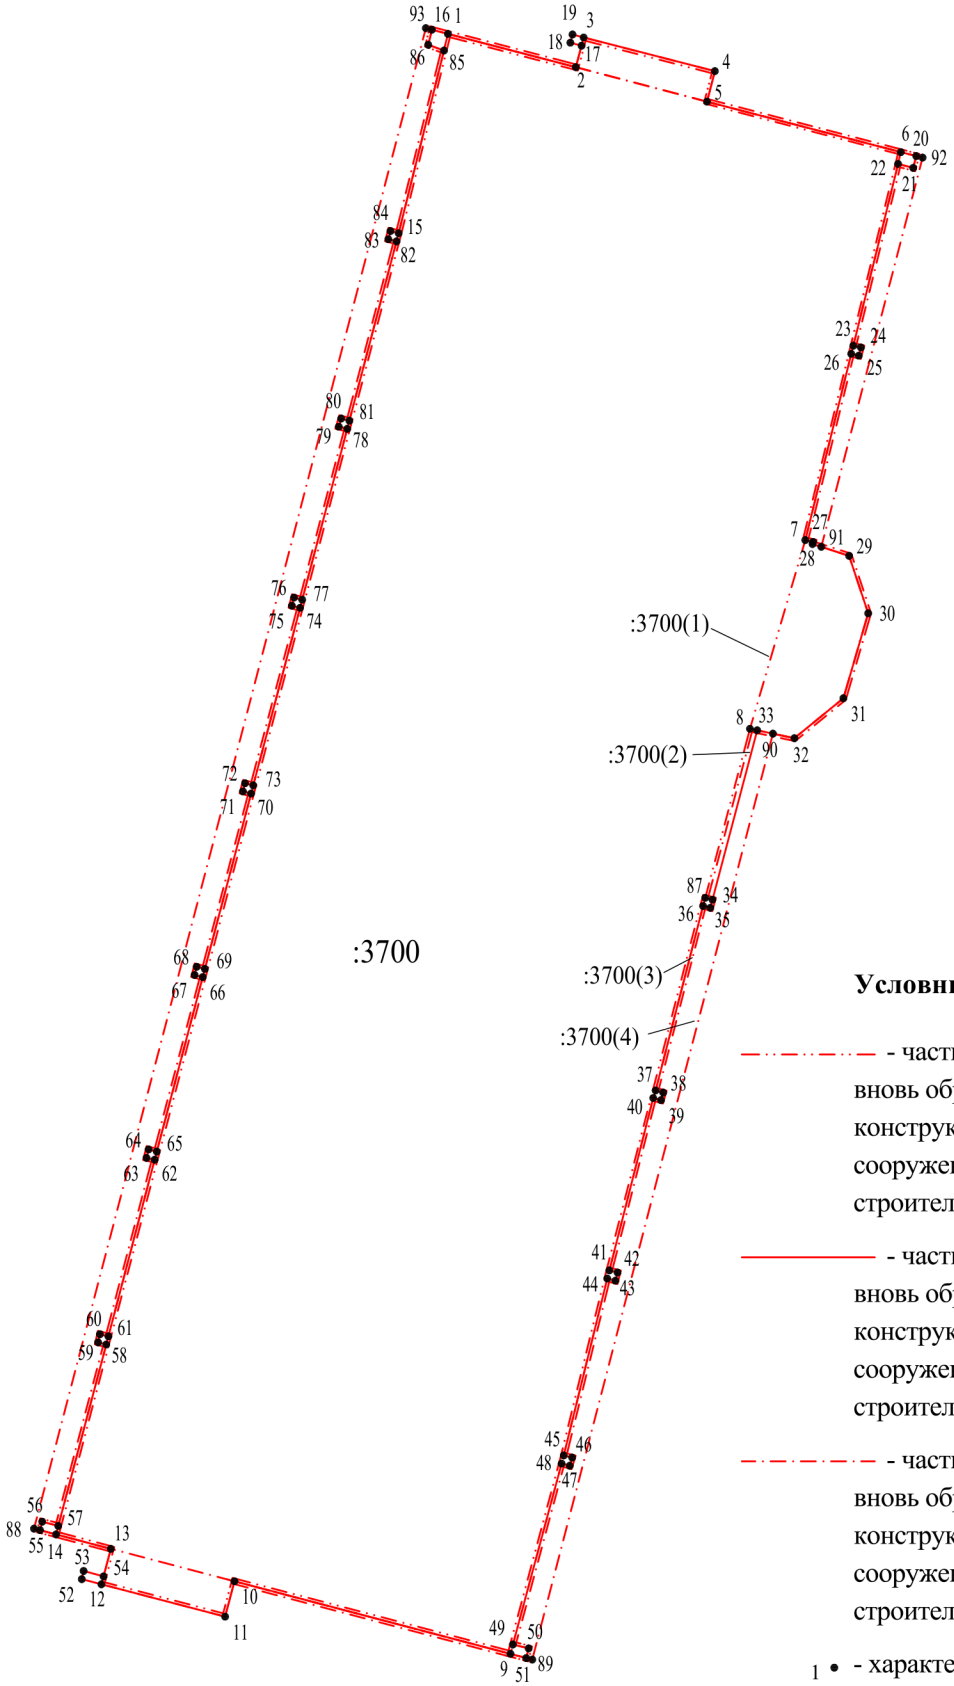

Условные обозначения:

- часть контура, образованного проекцией вновь образованного подземного конструктивного элемента здания, сооружения, объекта незавершенного строительства;

- часть контура, образованного проекцией вновь образованного наземного конструктивного элемента здания, сооружения, объекта незавершенного строительства;

- часть контура, образованного проекцией вновь образованного надземного конструктивного элемента здания, сооружения, объекта незавершенного строительства;

1 • - характерная точка контура здания;


:3700(1), :3700(2), :3700(3), :3700(4) - обозначение контура здания;

:3700 - кадастровый номер здания.

Масштаб 1:250

План этажа

Цокольный этаж

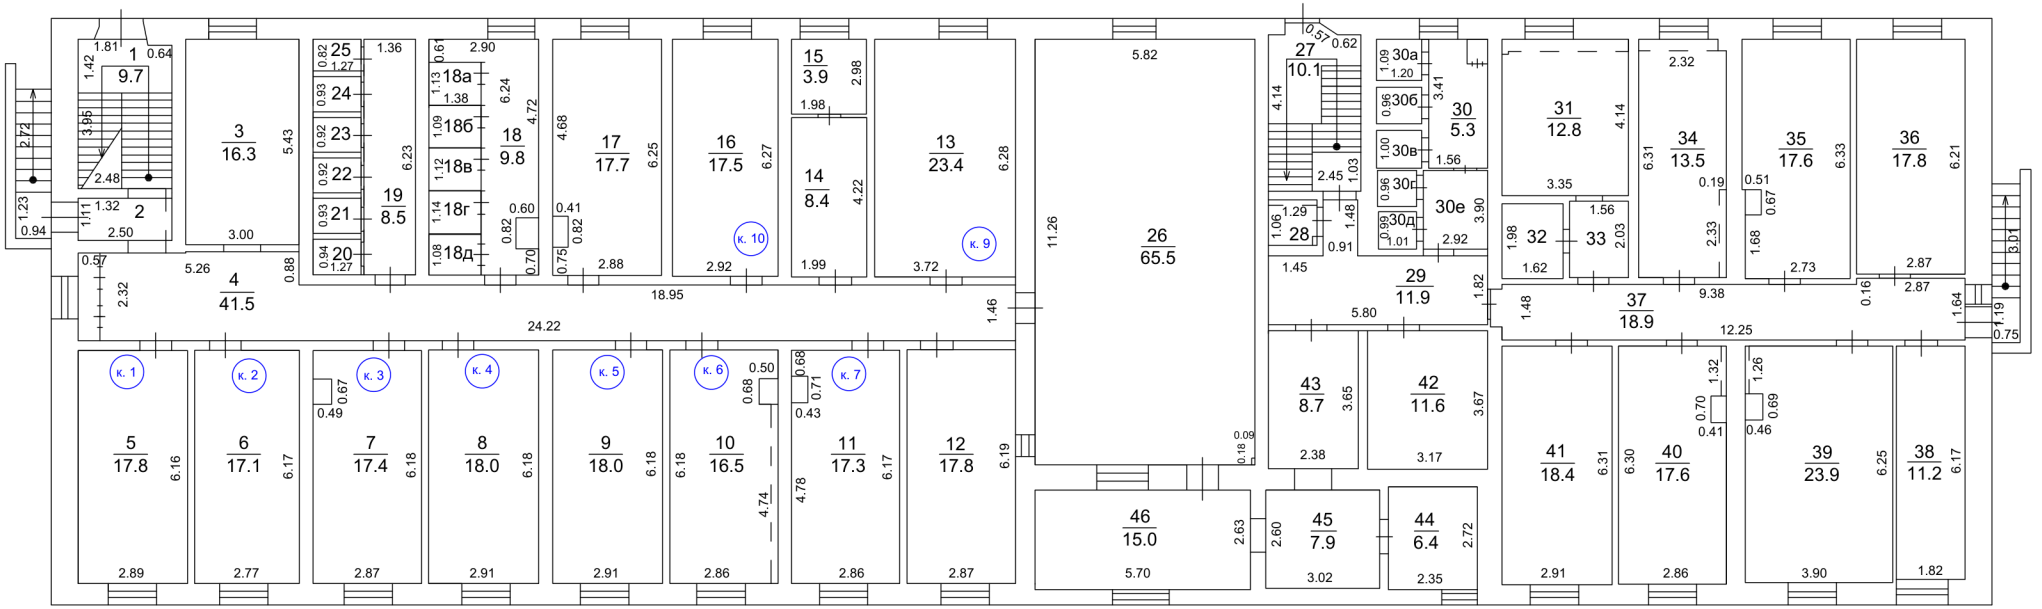


Условные обозначения:

- стена с окном и дверью
- линейный размер (3.50 / 5.00)
- номер помещения и площадь (1 / 15.6)
- лестница
- встроенные шкафы
- проём
- номер комнаты (к. 7)
- возвышения и ниши вдоль стен

План этажа

Первый этаж

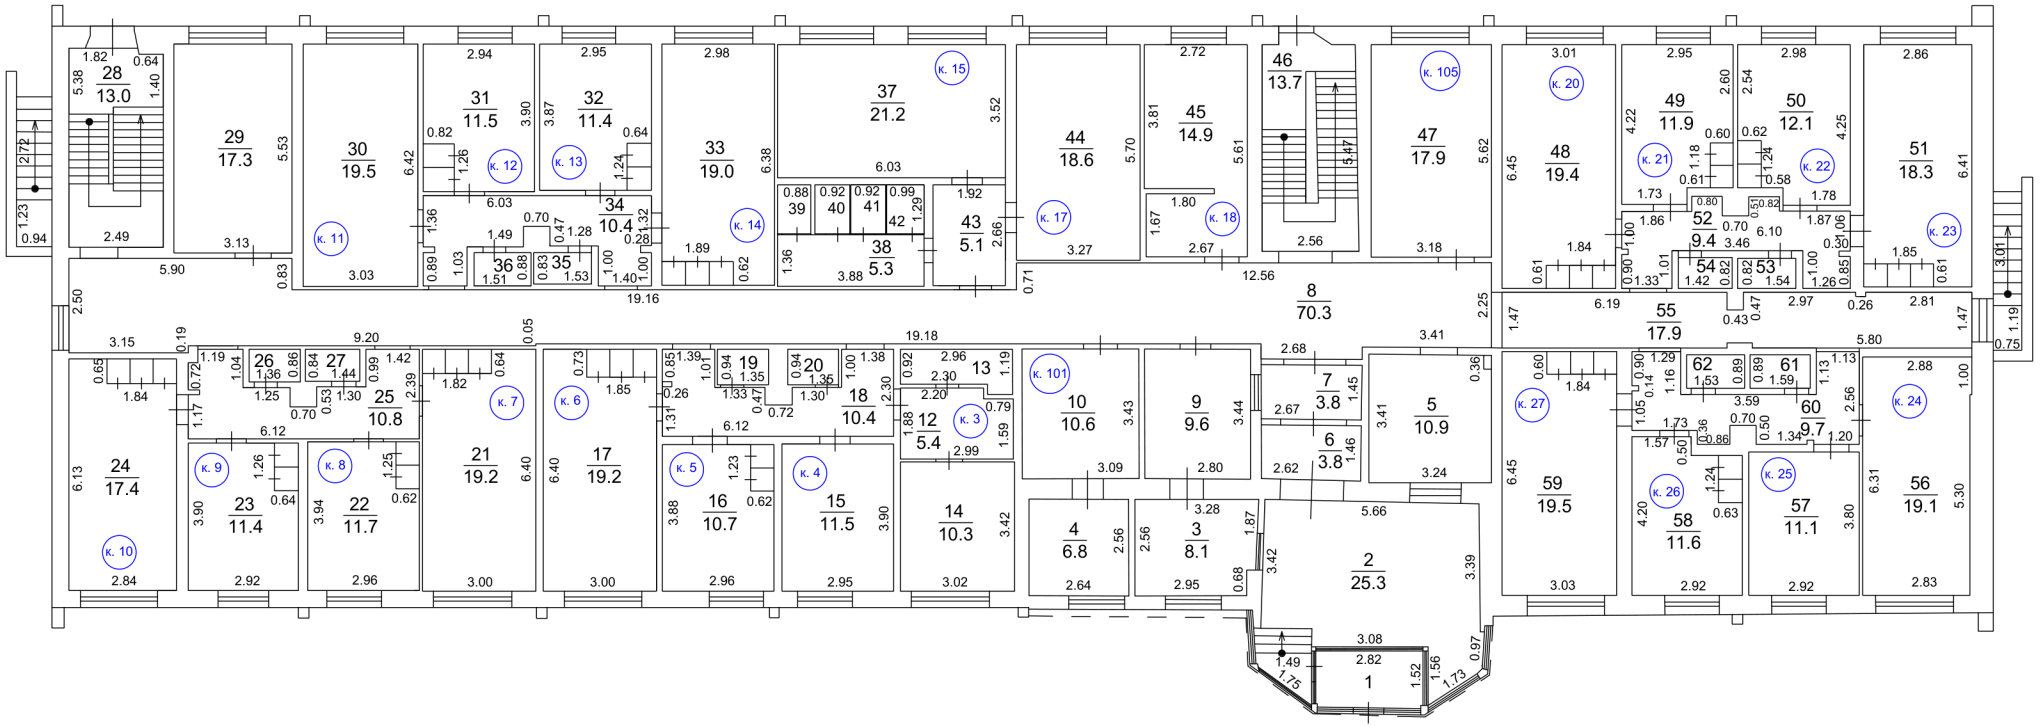


Условные обозначения:

- стена с окном и дверью
- 3.50 5.00 - линейный размер
- 1 / 15.6 - номер помещения и площадь
- лестница
- проем
- к. 7 - номер комнаты
- встроенные шкафы
- дверь с остеклением
- фундамент

План этажа

Второй этаж

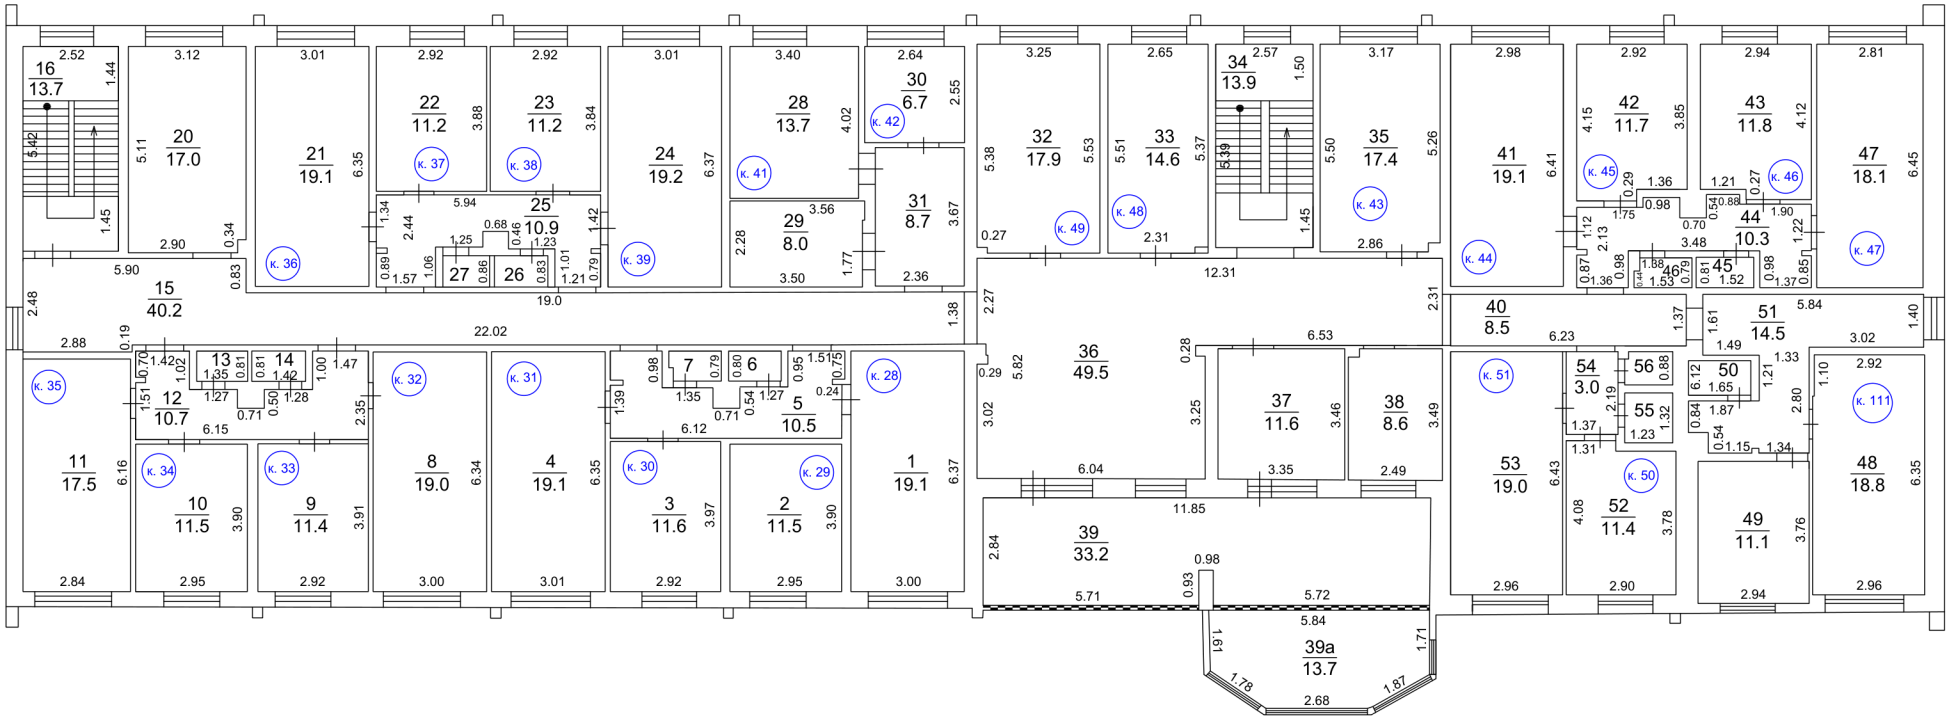


Условные обозначения:

- стена с окном и дверью
- 3.50 5.00 - линейный размер
- 1 / 15.6 - номер помещения и площадь
- лестница
- дверь с остеклением
- проем
- к. 7 - номер комнаты
- парапет лоджии

План этажа

Мансардный этаж

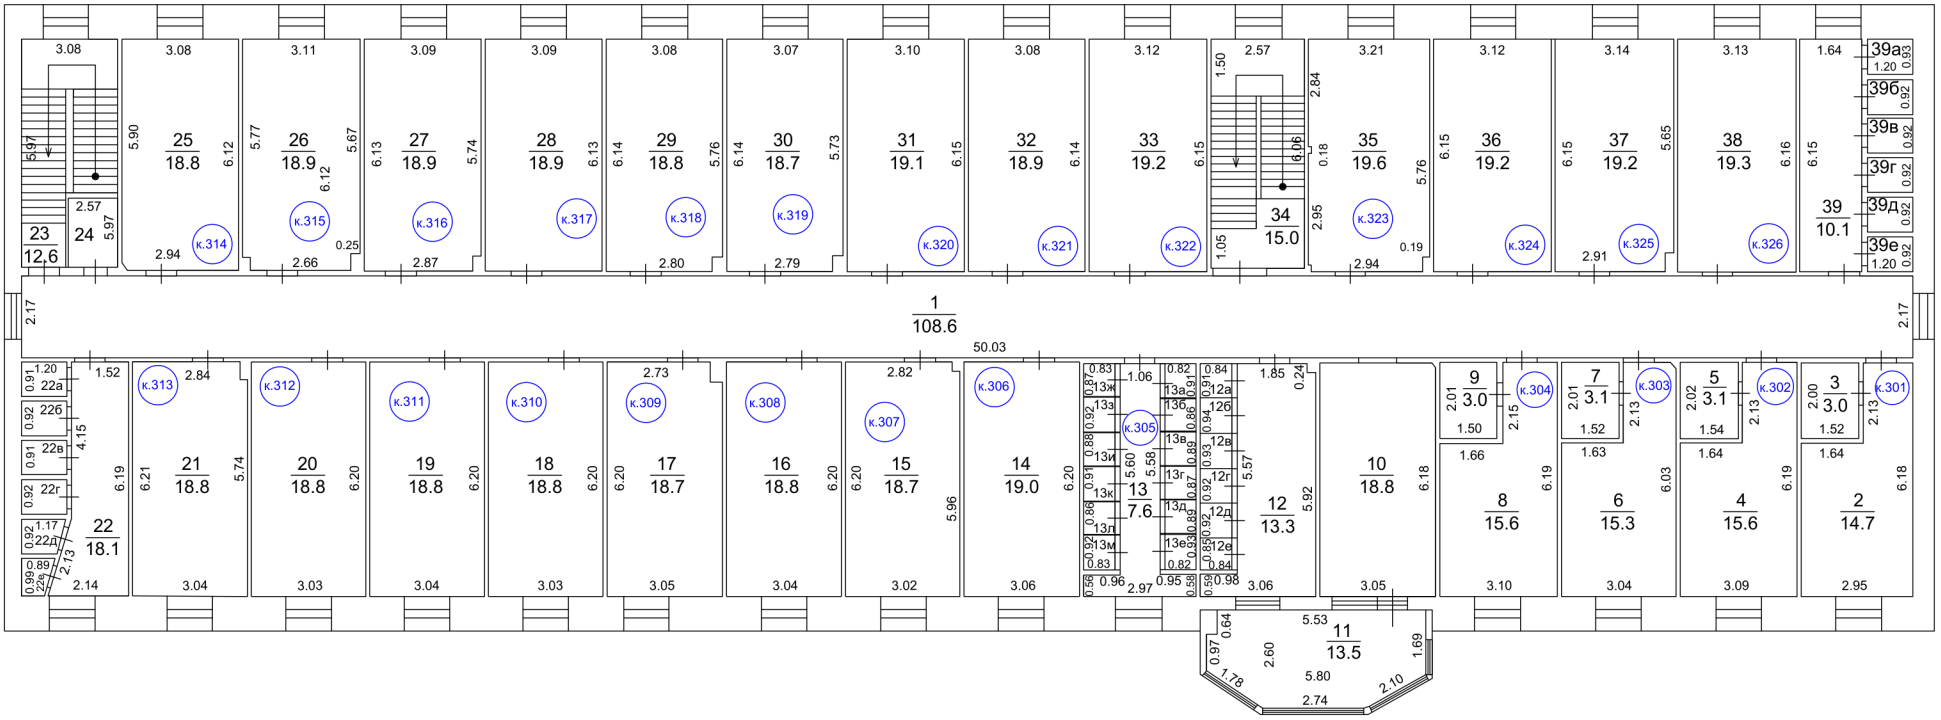

Условные обозначения:

- стена с окном и дверью
- линейный размер (3.50 5.00)
- номер помещения и площадь (1 / 15.6)
- лестница
- проем
- номер комнаты (к. 7)
- дверь с остеклением

Экспликация помещений в здании с кадастровым номером 50:22:0000000:3900, по адресу: Московская область, р-н Люберецкий, р.п. Малаховка, ул. Маяковского, д. 18

	Номер помещения на плане	*Номер комнаты*	*Наименование помещения*	*Общая площадь кв.м.*
Цокольный Этаж	2	-	тамбур	2.6
	3	-	прачечная	16.3
	4	-	коридор	41.5
	5	к.1	комната	17.8
	6	к.2	комната	17.1
	7	к.3	комната	17.4
	8	к.4	комната	18.0
	9	к.5	комната	18.0
	10	к.6	комната	16.5
	11	к.7	комната	17.3
	12	-	подсобное	17.8
	13	к.9	комната	23.4
	14	-	щитовая	8.4
	15	-	щитовая	3.9
	16	к.10	комната	17.5
	17	-	кухня	17.7
	18	-	санузел	9.8
	18а	-	душевая	1.6
	18б	-	душевая	1.5
	18в	-	душевая	1.5
	18г	-	душевая	1.6
	18д	-	душевая	1.5
	19	-	санузел	8.5
	20	-	туалет	1.2
	21	-	туалет	1.2
	22	-	туалет	1.2
	23	-	туалет	1.2
	24	-	туалет	1.2
	25	-	туалет	1.1
	26	-	прачечная, сушильная	65.5
	28	-	щитовая	1.3
	29	-	коридор	11.9
	30	-	санузел	5.3
	30а	-	душевая	1.3
	30б	-	душевая	1.5
	30в	-	душевая	1.2
	30г	-	туалет	1.0
	30д	-	туалет	1.0
	30е	-	санузел	3.5
	31	-	подсобное	12.8
	32	-	санузел	3.2
	33	-	подсобное	3.2
	34	-	комната	13.5
	35	-	комната	17.6
	36	-	комната	17.8
	37	-	коридор	18.9
	38	-	подсобное	11.2

	39	-	комната	23.9
	40	-	комната	17.6
	41	-	комната	18.4
	42	-	подсобное	11.6
	43	-	подсобное	8.7
	44	-	подсобное	6.4
	45	-	подсобное	7.9
	46	-	подсобное	15.0
	*Сумма площадей помещений по **цокольному** этажу*			**605.5**
	1	-	лестн. клетка	9.7
	27	-	лестн. клетка	10.1
	Площадь лестничных клеток			**19.8**
*Сумма площадей помещений по **цокольному** этажу (включая лестничные клетки)*				**625.3**
*Площадь **цокольному** этажа по внутренней поверхности наружных стен**				**720.7**
Первый этаж	1	-	тамбур	4.3
	2	-	коридор	25.3
	3	-	консьержная	8.1
	4	-	подсобное	6.8
	5	-	кухня	10.9
	6	-	коридор	3.8
	7	-	коридор	3.8
	8	-	коридор	70.3
	9	-	консьержная	9.6
	10	к.101	подсобное	10.6
	12	к.3	прихожая	5.4
	13	к.3	санузел	2.9
	14	к.3	комната	10.3
	15	к.4	комната	11.5
	16	к.5	комната	11.5
	17	к.6	комната	19.2
	18	-	коридор	10.4
	19	-	туалет	1.3
	20	-	туалет	1.3
	21	к.7	комната	19.2
	22	к.8	комната	11.7
	23	к.9	комната	11.4
	24	к.10	комната	17.4
	25	-	коридор	10.8
	26	-	туалет	1.2
	27	-	туалет	1.2
	29	-	кухня	17.3
	30	к.11	комната	19.5
	31	к.12	комната	11.5
	32	к.13	комната	11.4
	33	к.14	комната	19.0
	34	-	коридор	10.4
	35	-	туалет	1.3
	36	-	туалет	1.3
	37	к.15	комната	21.2
	38	-	санузел	5.3
	39	-	туалет	1.1

	40	-	душевая	1.2
	41	-	душевая	1.2
	42		душевая	1.3
	43	-	коридор	5.1
	44	к.17	комната	18.6
	45	к.18	комната	14.9
	47	к.105	комната	17.9
	48	к.20	комната	19.4
	49	к.21	комната	11.9
	50	к.22	комната	12.1
	51	к.23	комната	18.3
	52	-	коридор	9.4
	53	-	туалет	1.2
	54	-	туалет	1.2
	55	-	коридор	17.9
	56	к.24	комната	19.1
	57	к.25	комната	11.1
	58	к.26	комната	11.6
	59	к.27	комната	19.5
	60	-	коридор	9.7
	61	-	туалет	1.4
	62	-	туалет	1.4
	*Сумма площадей помещений по **первому** этажу*			**644.9**
	28	-	лестн. клетка	13.0
	46	-	лестн. клетка	13.7
	Площадь лестничных клеток			**26.7**
*Сумма площадей помещений по **первому** этажу (включая лестничные клетки)*				**671.6**
*Площадь **первого** этажа по внутренней поверхности наружных стен**				**746.4**
Второй этаж	1	к.28	комната	19.1
	2	к.29	комната	11.5
	3	к.30	комната	11.6
	4	к.31	комната	19.1
	5	-	коридор	10.5
	6	-	туалет	1.1
	7	-	туалет	1.1
	8	к.32	комната	19.0
	9	к.33	комната	11.4
	10	к.34	комната	11.5
	11	к.35	комната	17.5
	12	-	коридор	10.7
	13	-	туалет	1.1
	14	-	туалет	1.2
	15	-	коридор	40.2
	20	-	кухня	17.0
	21	к.36	комната	19.1
	22	к.37	комната	11.2
	23	к.38	комната	11.2
	24	к.39	комната	19.2
	25	-	коридор	10.9
	26	-	туалет	1.2
	27	-	туалет	1.0
	28	к.41	комната	13.7
	29	-	электрощитовая	8.0

	30	к.42	комната	6.7
	31	-	коридор	8.7
	32	к.49	комната	17.9
	33	к.48	комната	14.6
	35	к.43	комната	17.4
	36	-	коридор	49.5
	37	-	комната	11.6
	38	-	кухня	8.6
	39	-	лоджия	33.2
	39а	-	лоджия	13.7
	40	-	коридор	8.5
	41	к.44	комната	19.1
	42	к.45	комната	11.7
	43	к.46	комната	11.8
	44	-	коридор	10.3
	45	-	туалет	1.2
	46	-	туалет	1.1
	47	к.47	комната	18.1
	48	к.111	комната	18.8
	49	-	комната	11.1
	50	-	туалет	1.5
	51	-	коридор	14.5
	52	к.50	комната	11.4
	53	к.51	комната	19.0
	54	-	коридор	3.0
	55	-	санузел	1.7
	56	-	туалет	1.1
	*Сумма площадей помещений по **второму** этажу*			**644.9**
	16	-	лестн. клетка	13.7
	34	-	лестн. клетка	13.9
	Площадь лестничных клеток			**27.6**
*Сумма площадей помещений по **второму** этажу (включая лестничные клетки)*				**672.5**
*Площадь **второго** этажа по внутренней поверхности наружных стен**				**747.5**
Мансардный этаж	1	-	коридор	108.6
	2	к.301	комната	14.7
	3	-	санузел	3.0
	4	к.302	комната	15.6
	5	-	санузел	3.1
	6	к.303	комната	15.3
	7	-	санузел	3.1
	8	к.304	комната	15.6
	9	-	санузел	3.0
	10	-	кухня	18.8
	11	-	лоджия	13.5
	12	-	санузел	0.8
	12а	-	душевая	0.8
	12б	-	душевая	0.8
	12в	-	душевая	0.8
	12г	-	душевая	0.8
	12д	-	душевая	0.8
	12е	-	душевая	0.7
	13	к.305	санузел	7.6
	13а	-	душевая	0.7

	13б	-	душевая	0.7
	13в	-	душевая	0.7
	13г	-	душевая	0.7
	13д	-	душевая	0.7
	13е	-	душевая	0.8
	13ж	-	душевая	0.7
	13з	-	душевая	0.8
	13и	-	душевая	0.7
	13к	-	душевая	0.8
	13л	-	душевая	0.7
	13м	-	душевая	0.8
	14	к.306	комната	19.0
	15	к.307	комната	18.7
	16	к.308	комната	18.8
	17	к.309	комната	18.7
	18	к.310	комната	18.8
	19	к.311	комната	18.8
	20	к.312	комната	18.8
	21	к.313	комната	18.8
	22	-	санузел	18.1
	22а	-	туалет	1.1
	22б	-	туалет	1.1
	22в	-	туалет	1.0
	22г	-	туалет	1.1
	22д	-	туалет	1.0
	22е	-	туалет	0.7
	24	-	подсобное	2.4
	25	к.314	комната	18.8
	26	к.315	комната	18.9
	27	к.316	комната	18.9
	28	к.317	комната	18.9
	29	к.318	комната	18.8
	30	к.319	комната	18.7
	31	к.320	комната	19.1
	32	к.321	комната	18.9
	33	к.322	комната	19.2
	35	к.323	комната	19.6
	36	к.324	комната	19.2
	37	к.325	комната	19.2
	38	к.326	комната	19.3
	39	-	санузел	10.1
	39а	-	туалет	1.1
	39б	-	туалет	1.1
	39в	-	туалет	1.1
	39г	-	туалет	1.1
	39д	-	туалет	1.1
	39е	-	туалет	1.1
	*Сумма площадей помещений по **мансардному** этажу*			**677.3**
	23	-	лестн. клетка	12.6
	34	-	лестн. клетка	15.0
	Площадь лестничных клеток			**27.6**
*Сумма площадей помещений по **мансардному** этажу (включая лестничные клетки)*				**704.9**
*Площадь **мансардного** этажа по внутренней поверхности*				**752.8**

*наружных стен**	
ИТОГО:	
Сумма площадей помещений по зданию	**2572.6**
Сумма площадей помещений по зданию (включая лестничные клетки)	**2674.3**
ОБЩАЯ ПЛОЩАДЬ ЗДАНИЯ по внутренней поверхности наружных стен *	**2967.4**

**Согласно п.10.2. Требований к определению площади здания, сооружения и помещения, машино-места утверждѐнных Приказом Росреестра от 23.10.2020 № П/0393, площадь этажа нежилого здания определяется в пределах внутренних поверхностей наружных стен.*

Согласно п.5 Требований, площадь нежилого или жилого здания, сооружения определяется как сумма площадей всех надземных и подземных этажей (включая технический, мансардный, цокольный и иные), а также эксплуатируемой кровли.

В данной экспликации указаны как площади комнат, расположенных в здании, так и общая площадь здания, установленная в соответствии с Требованиями по внутренней поверхности наружных стен.

Разница между общей площадью здания и суммой площадей всех комнат, расположенных в здании, является площадью, занятой внутренними стенами и перегородками.